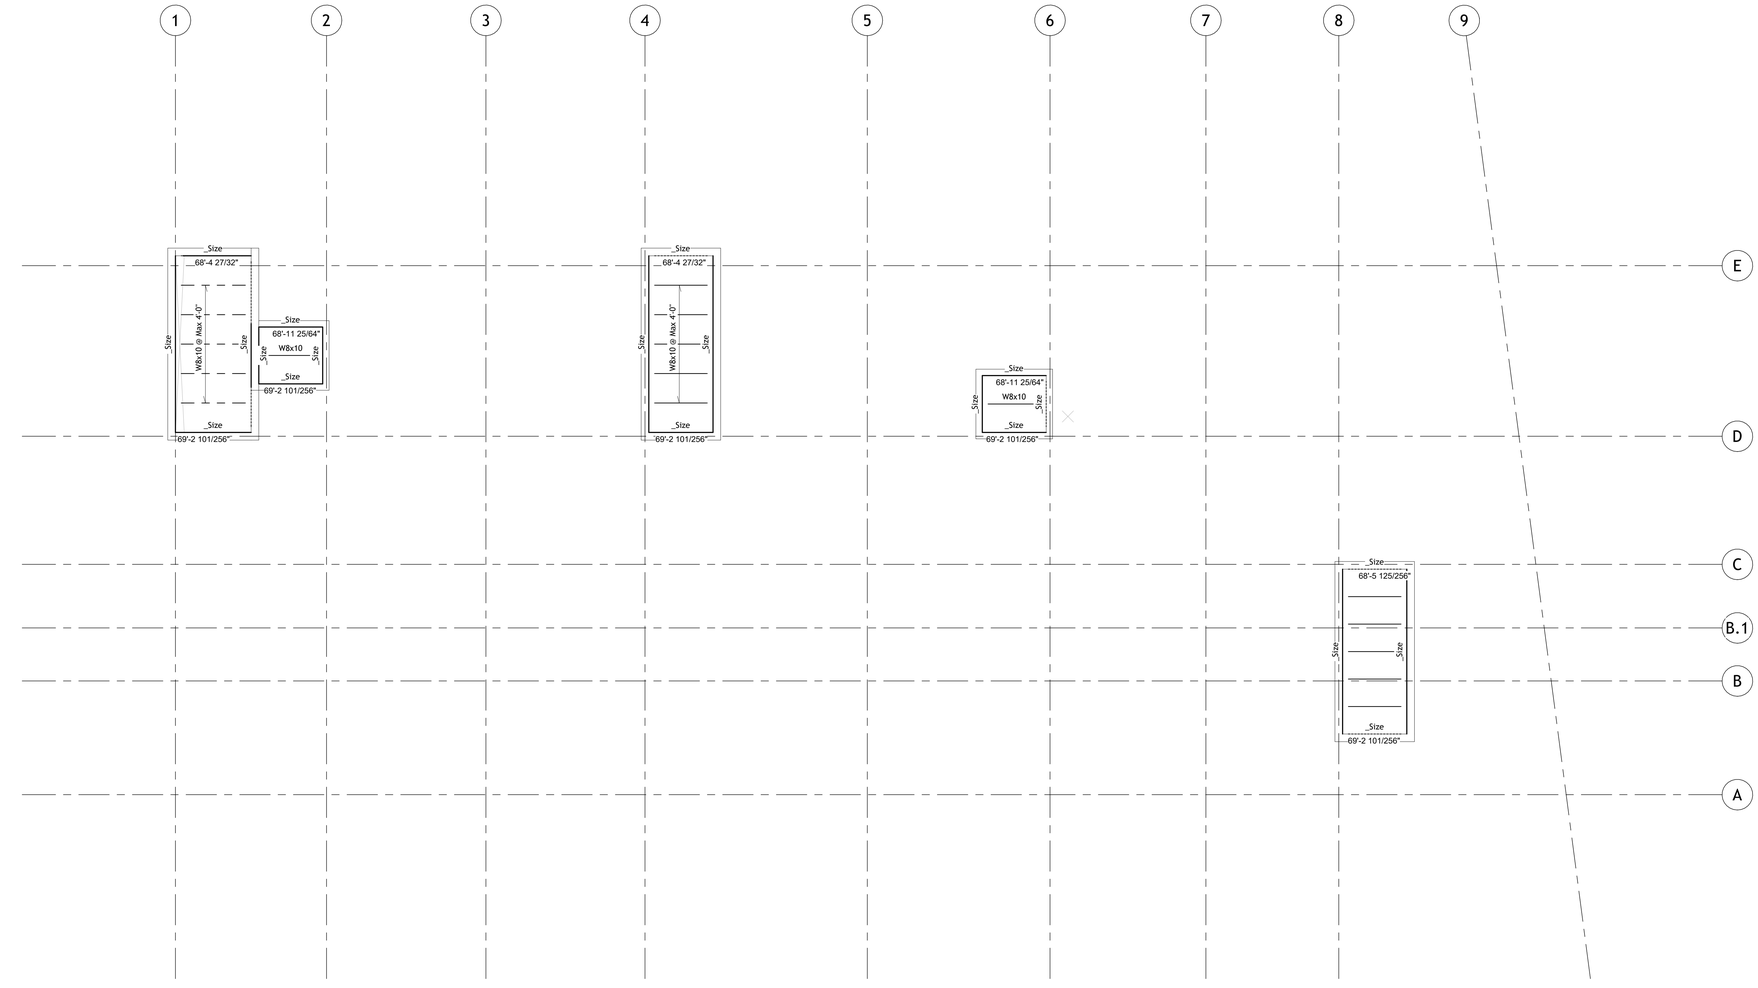


1 Parapet 2
1/8" = 1'-0"

NOT FOR CONSTRUCTION

AUTODESK

www.autodesk.com/revit

Project Management & Architectural Modeling:

Cartesian Inverse, PA
Chicago, IL 28246

Architectural Design:

Etienne Oiseau, LLC
Detroit, MI 96435

Structural Design and Modeling:

Safe Harbor Engineering, PC
11 Eleventh Street, Suite 11
Purchasing Decisions, NO 13131-1525

MEP Design and Modeling:

Droffats Consulting Services, LLC
Los Angeles, CA 78383

Civil Engineering:

Rubicon Engineering Solutions, INC
Pittsburgh, PA 77462-5247

Landscape Architecture & Community Planning :

Dagny Taggart, LTD
Brownsville, PA 52872

Commercial Kitchen Design:

Designing Trends
103B Broadway
Knoxville, TN 36664-2084

No.	Description	Date
	Not For Construction	
1	Snowdon Towers 2.0	Feb 15

Autodesk Snowdon Towers 2.0

Stair Towers

Project Number	7765328-33-S-2.0
Date	2/6/2026
Drawn By	SHE
Checked By	ADSK

S108

Scale 1/8" = 1'-0"

8/5/2026 7:51:25 PM