Structural Connection Schedule

Type	Beam/Column Types	Count
Base plate		
Base plate W10	W10x49	5
Base plate W10	W14x109	5
Base plate W14 and W18	W10x49	6
Base plate W14 and W18	W14x109	12
Base plate W14 and W18	W18x119	2
BM W18x55 to W10x49 Web		
BM W18 to W10 Web	W10x49, W18x55	5
BM W18 to W10 Web	W10x49, W18x86	2
BM W18x55 to W14x109 -5		
BM W18 to W14 Web -5	W14x109, W18x55	3
BM W18x55 to W14x109 Web		
BM W18 to W14 Web	W10x49, W18x55	1
BM W18 to W14 Web	W14x109, W18x55	10
BM W18 to W14 Web	W14x109, W18x86	2
BM W18 to W14 Web -2.5"	W14x109, W18x55	9
Clip angle		
Clip angle	W10x49, W30x235	2
Clip angle	W18x119, W36x232	2

Structural Connection Schedule


Type	Beam/Column Types	Count
Clip angle - skewed		
Clip angle - skewed 2	W8x10, W8x10	2
Clip angle - skewed 2	W12X26, W8x10	3
Clip angle - skewed 2	W18x55, W8x10	4
Clip angle - skewed 2	W18x86, W8x10	13
Clip angle - skewed 2	W18x119, W8x10	2
Clip angle - skewed 2	W30x235, W8x10	5
Clip angle - skewed 3	W18x86, W12X26	1
Clip angle - skewed 3	W18x86, W18x86	1
Clip angle - skewed 3 Bottom	W30x235, W12X26	5
Clip angle - skewed 4	W18x86, W18x86	5
Custom Connection		
BM W18x86 to W18x119 Web	W18x119, W18x55	2
BM W18x86 to W18x119 Web	W18x119, W18x86	2
BM W18x86 to W18x119 Web Offset	W18x119, W18x55	1

Structural Connection Schedule

Type	Beam/Column Types	Count
Embed beam seat		
Embed beam seat	W18x55	11
End Bearing Plate W18x55		
End Bearing Plate W18	W18x55	15
End Bearing Plate W18	W18x86	2
Front plate splice		
1' 2" x 1' 8"	W14x109, W10x49	1
1' 2" x 1' 8"	W18x119, W10x49	2
Shear plate		
BM to BM 3 Bolt	W18x55, W16X26	10
BM to BM 3 Bolt	W18x86, W16X26	10
BM to BM 4 Bolt	W18x55, W18x55	6
BM to BM 4 Bolt	W18x86, W18x55	2
BM to Col Flange 4 Bolt	W10x49, W18x55	4
BM to Col Flange 4 Bolt	W10x49, W18x86	8
BM to Col Flange 4 Bolt	W14x109, W18x55	7
Shear plate 2	W12X26, W8x10	3
Shear plate 2	W18x86, W8x10	26


Structural Connection Schedule

Type	Beam/Column Types	Count
Shear Plate 2 with Extension		
Shear Plate 2 with Extension	W12X26, W12X26	6
Stiffener		
Stiffener 2 Sides	W10x49	2
Stiffener 2 Sides	W18x55	11
Stiffener 2 Sides	W18x119	4
Stiffener 2 Sides	W36x232	10

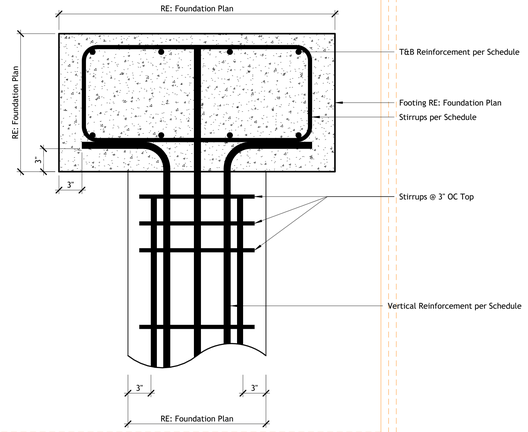


1 Drilled Pier at Continious Footing
1 1/2" = 1'-0"

Use the Global Parameter "Turn off for Plot" to hide all the alignment lines in the detail box:

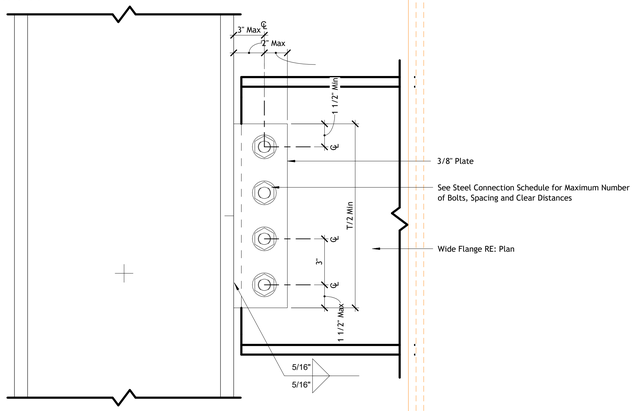

5 Beam to Column Connection
3" = 1'-0"

Use the Global Parameter "Turn off for Plot" to hide all the alignment lines in the detail box:

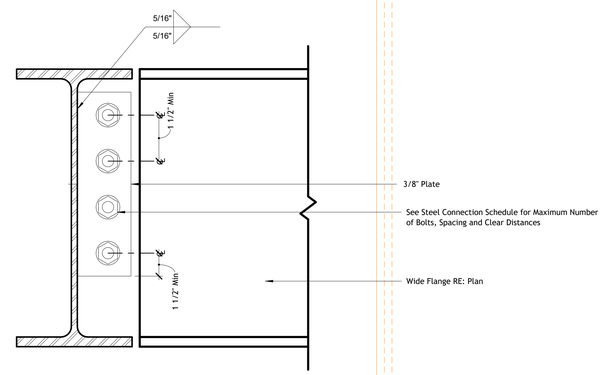


6 Beam to BeamConnection
3" = 1'-0"

Use the Global Parameter "Turn off for Plot" to hide all the alignment lines in the detail box:

Not Used

2 Not Used
1 1/2" = 1'-0"


Use the Global Parameter "Turn off for Plot" to hide all the alignment lines in the detail box:
The Show Hidden command was used to display the beam behind the plate:

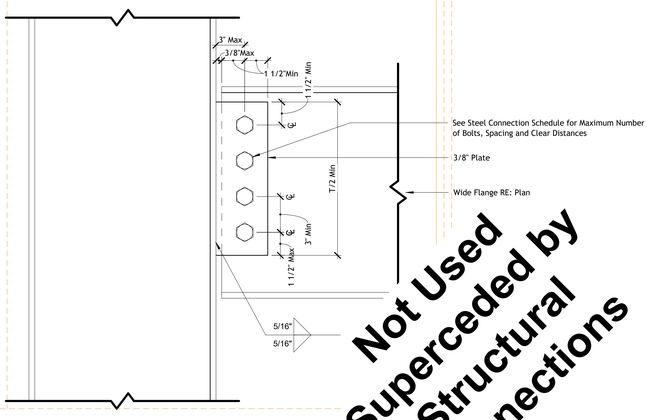

Not Used
Superceded by Structural Connections

4 Beam to Column Connection
3" = 1'-0"

Use the Global Parameter "Turn off for Plot" to hide all the alignment lines in the detail box:
The Show Hidden command was used to display the beam behind the plate:

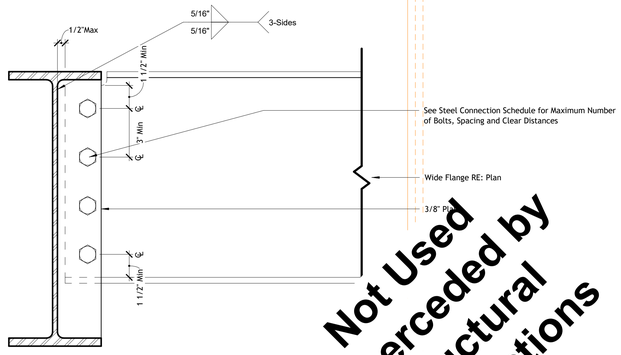

Not Used
Superceded by Structural Connections

3 Beam to Beam Connection
3" = 1'-0"

NOT FOR CONSTRUCTION

AUTODESK

www.autodesk.com/revit

Project Management & Architectural Modeling:

Cartesian Inverse, PA
Chicago, IL 28246

Architectural Design:

Etienne Oiseau, LLC
Detroit, MI 96435

Structural Design and Modeling:

Safe Harbor Engineering, PC
11 Eleventh Street, Suite 11
Purchasing Decisions, NO 13131-1525

MEP Design and Modeling:

Droffats Consulting Services, LLC
Los Angeles, CA 78383

Civil Engineering:

Rubicon Engineering Solutions, INC
Pittsburgh, PA 77462-5247

Landscape Architecture & Community Planning:

Dagny Taggart, LTD
Brownsville, PA 52872

Commercial Kitchen Design:

Designing Trends
103B Broadway
Knoxville, TN 36664-2084

No.	Description	Date
	Not For Construction	
1	Snowdon Towers 2.0	Feb 15

Autodesk Snowdon Towers 2.0

Details

Project Number	7765328-33-S-2.0
Date	2/6/2026
Drawn By	SHE
Checked By	ADSK

S600

Scale: As indicated

8/5/2026 7:51:26 PM